

Date 2025-06-28

Instr. FS

BS

Notes/Sketch

Page 1 of

Station △	Fort Stanton Cave Study Project			L	R	U	D	Notes (Feet or meters, declination, IH/LH, photographer, leads, water, etc.)
	Distance ←→	Azimuth ↻	Inclination ↙	←	→	↑	↓	
MK64	21.43	FS	PS -13.8			12	4	
ML1	38.1	BS	PS 0.6			1/3	1	
ML2	32.27	BS	PS 1.2			1.5	1	
ML3	56.51	BS	PS 1.5			.5	2	
4	35.88	BS	PS 4.0			2	1	
5	39.62	BS	PS 0.2			2	4	
6	91.70	BS	PS 0.3			0.5	5.5	
7	71.05	BS	PS 0.2			2.5	2.5	
8	30.80	BS	PS 5.4			2.5	0	
9	24.01	BS	PS 12.2			2.5	0	
MK68	11.10	BS	PS 27.4			7	5	
ML10	24.54	BS	PS -2.4			47	5	
ML11	19.47	BS	PS -0.9			29	0	
ML12	35.8	BS	PS 6.6			12	2.5	
ML13		BS	PS			3	3	
		BS	PS					
		BS	PS					
		BS	PS					
	Total survey on this page							




Scale: 1" = 40'

☐ Plan
☒ Profile

Date

Area

Sketcher Alex Fischer Page 2 of

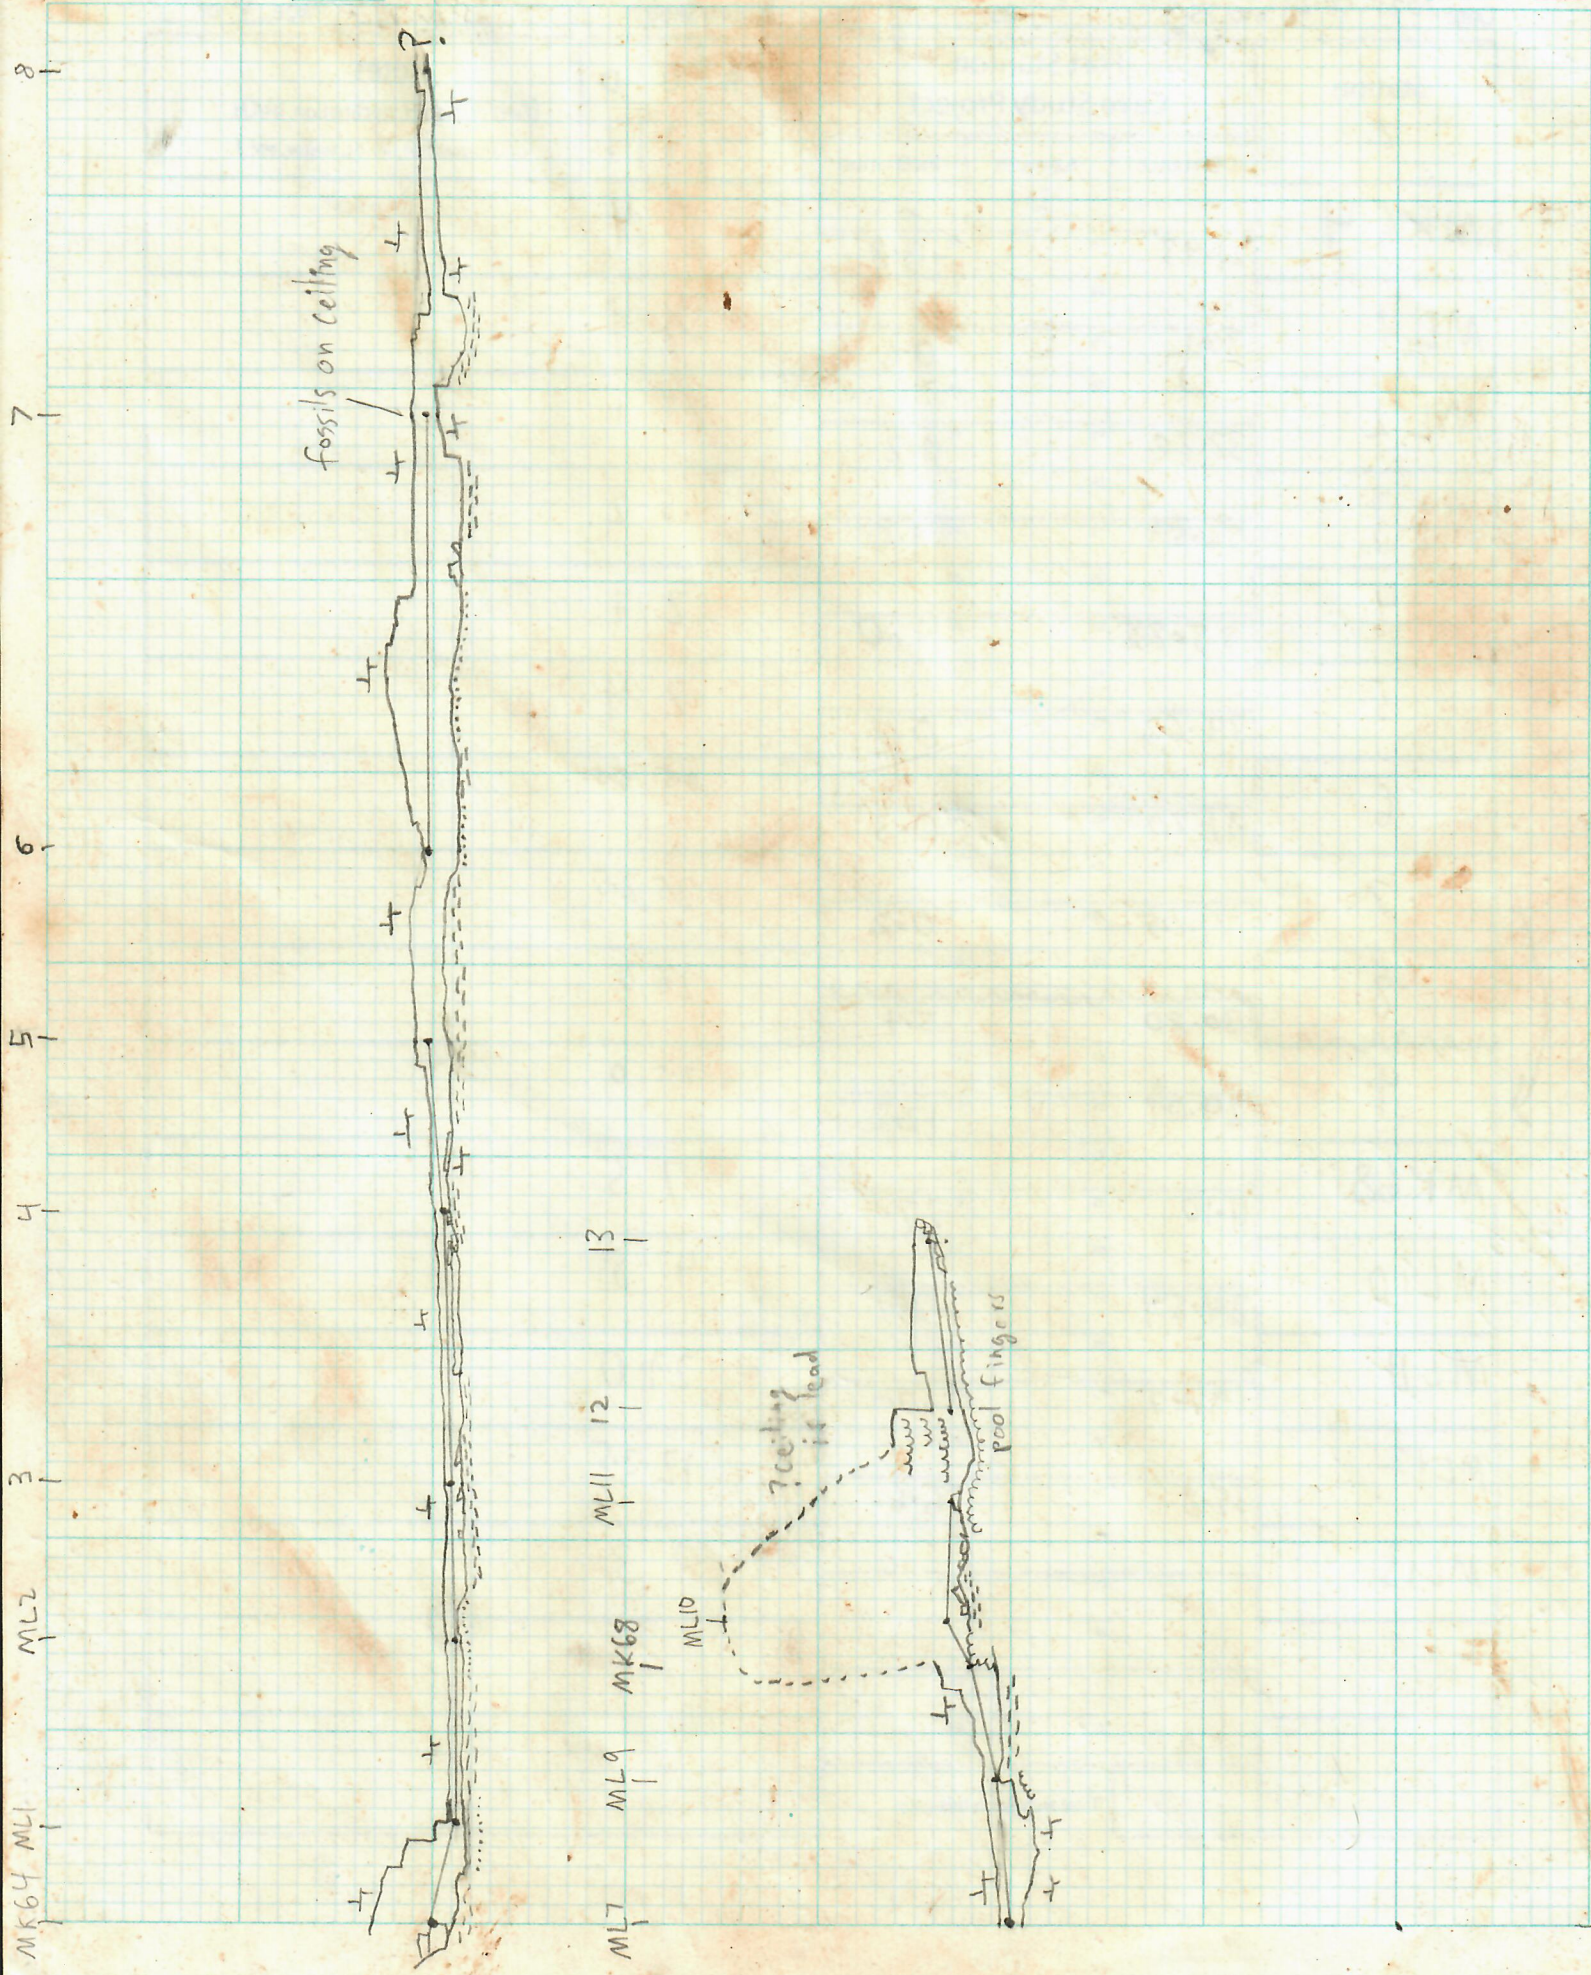

Date 2025-06-28


Instr. FS

BS

Notes/Sketch Alex Fischer

Page 3 of

Station △	Fort Stanton Cave Study Project			L	R	U	D	Notes (Feet or meters, declination, IH/LH, photographer, leads, water, etc.)
	Distance ↔	Azimuth ↻	Inclination ↙	←	→	↑	↓	
ML8	70.64	FS	FS -0.1			2.5	0	
ML14	25.05	BS	BS -5.9			1	0.5	
ML15	50.97	FS	FS 0.7			2	1	
16	40	BS	BS -1			3	1	
17	63.06	FS	FS 0.7			1.5	1.5	
18	63.41	BS	BS 1.2			2	1.5	
19	29.77	FS	FS 7.1			5	2	
20	30.15	BS	BS 0.5			20	3.5	
21	56.77	FS	FS 0.4			3.5	3	
22	56.21	BS	BS 4.9			3	2	
23	80.72	FS	FS -2.5			1	3	
24	50.58	BS	BS 2.2			7	5	
25	57.30	FS	FS 1.5			1	4	
26	47.83	BS	BS -0.7			2	1.5	
27	72.35	FS	FS 0.1			2.5	4	
28		BS	BS					
		FS	FS					
		BS	BS					
Total survey on this page								

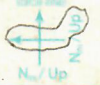


Scale: 1" = 40'

☐ Plan
☒ Profile

Date 2025-06-28 Area

Sketcher Alex Fischer

Page 4 of

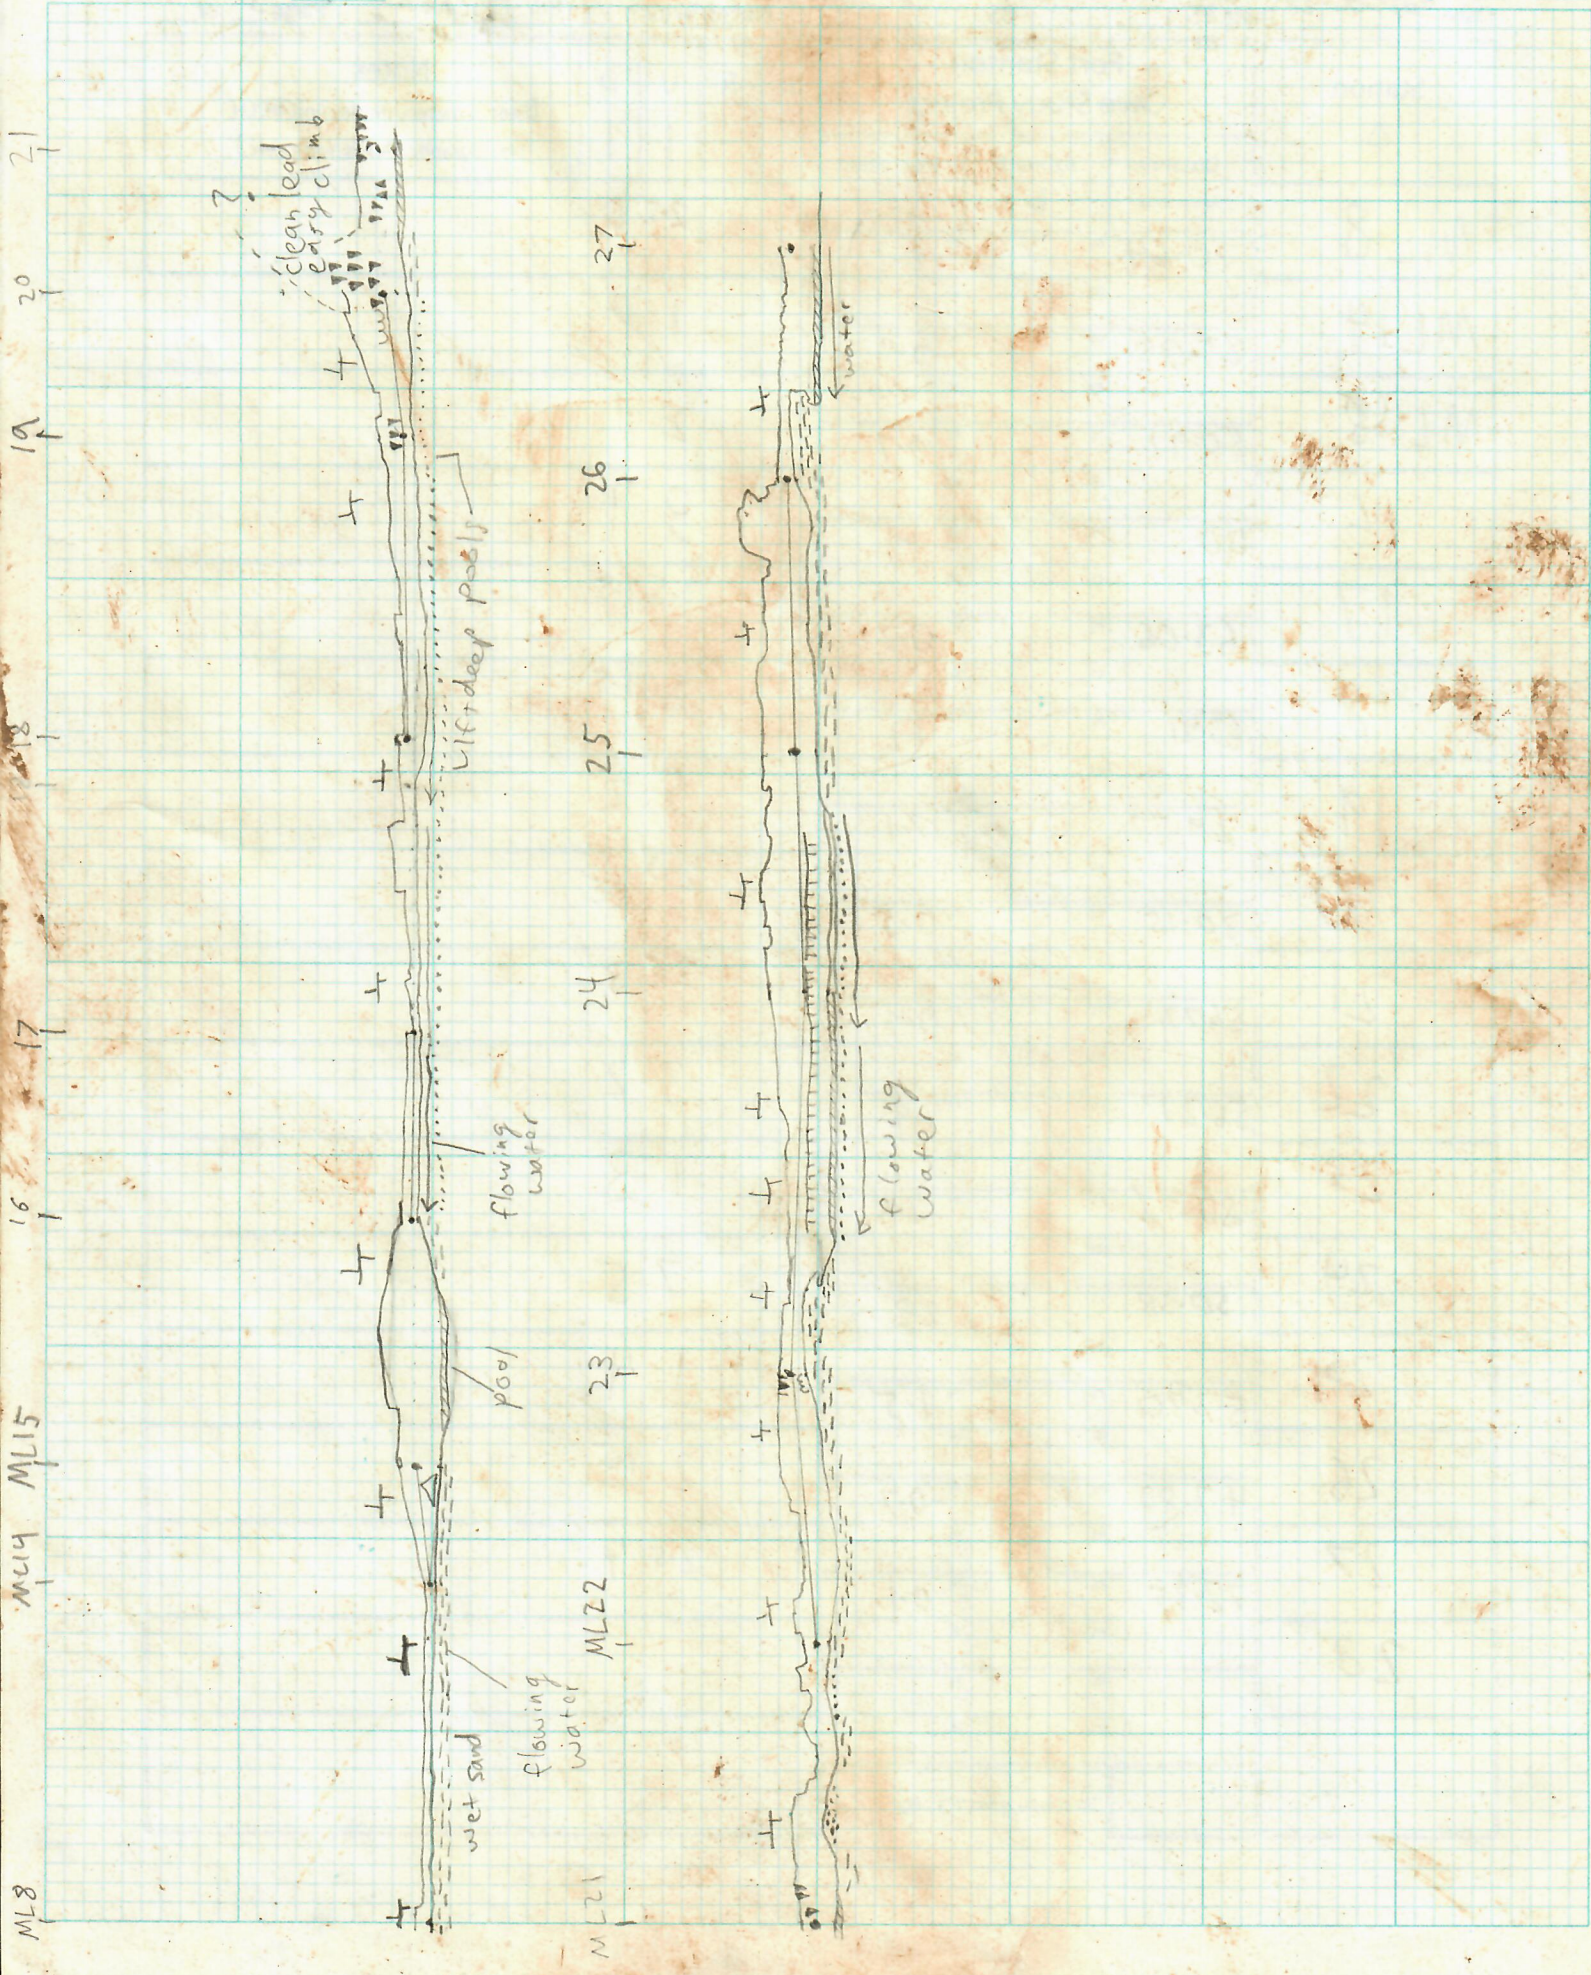



Scale: 1" =

40'

☐ Plan
☒ Profile

Date

Area

Sketcher

Alex Fischer

Page 6 of

